# ПРОЕКТНАЯ ДОКУМЕНТАЦИЯ Индивидуальный жилой дом

по адресу: г. Анапа, с. Супсех, ул. Левинского, 3

Эскизный проект
"Архитектурные решения"
130422-АР



### Ведомость листов комплекта марки АР. Наименование Лист Примечание 1 Общие данные. 2 3D визуализация 3 3D визуализация Генплан 4 План первого, второго этажа. Мебель 5 6 План первого, второго этажа. Кладочный 7 План кровли Фасад 1-6, 6-1 8 9 Фасад А-Ж, Ж-А 10 Paspes 1-1, 2-2 11 Разрез 3-3

#### Общие указания.

- 1. Проектная документация по объекту «Индивидуальный жилой дом» разработан в стадии "Эскиз" на основании задания на проектирования, утвержденного заказчиком.
- 2. Проект предназначен для строительства в III Б климатическом районе.
- 3. Степень огнестойкости здания II.

Класс здания по функциональной пожарной опасности Ф1.3.

- 4. За нулевую отметку принят уровень чистого пола 1 этажа.
- 5. Наружные стены 2-х слойные выполнены из блоков, толщиной 320 мм., утеплитель 80 мм.
- 6. Отделка фасадов.

Наружные стены - декор. штукатурка.

Цоколь - облицовка керамогранитными плитками.


Кровля - плоская

Окна и витражи - металлопластиковые.


#### Основные строительные показатели.

	Наименование	Площадь, м2				Стрительный объем, м3			
		площадь застройки	общая площадь здания			подземная часть	надземная часть	общий	
	Жилой дом	180,0				0			


		Индивидуальный жилой дом по адресу: с. Супскх, ул. Левинского, З	130422-AP		P
Архитектор	Ткачев		Стадия	Лист	Листов
		Жилой дом	АC	1	
		Общие данные			

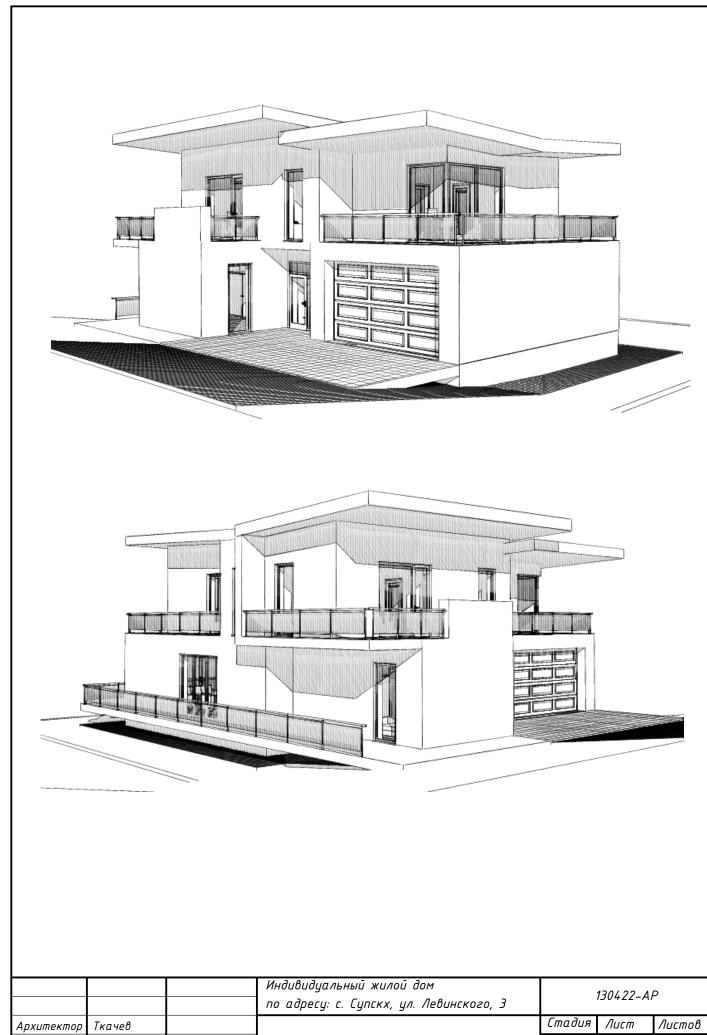


		Индивидуальный жилой дом по адресу: с. Супскх, ул. Левинского, З	130422-AP		Ρ
Архитектор	Ткачев		Стадия	Лист	Листов
		Жилой дом	АC	2	
		Визуализация			

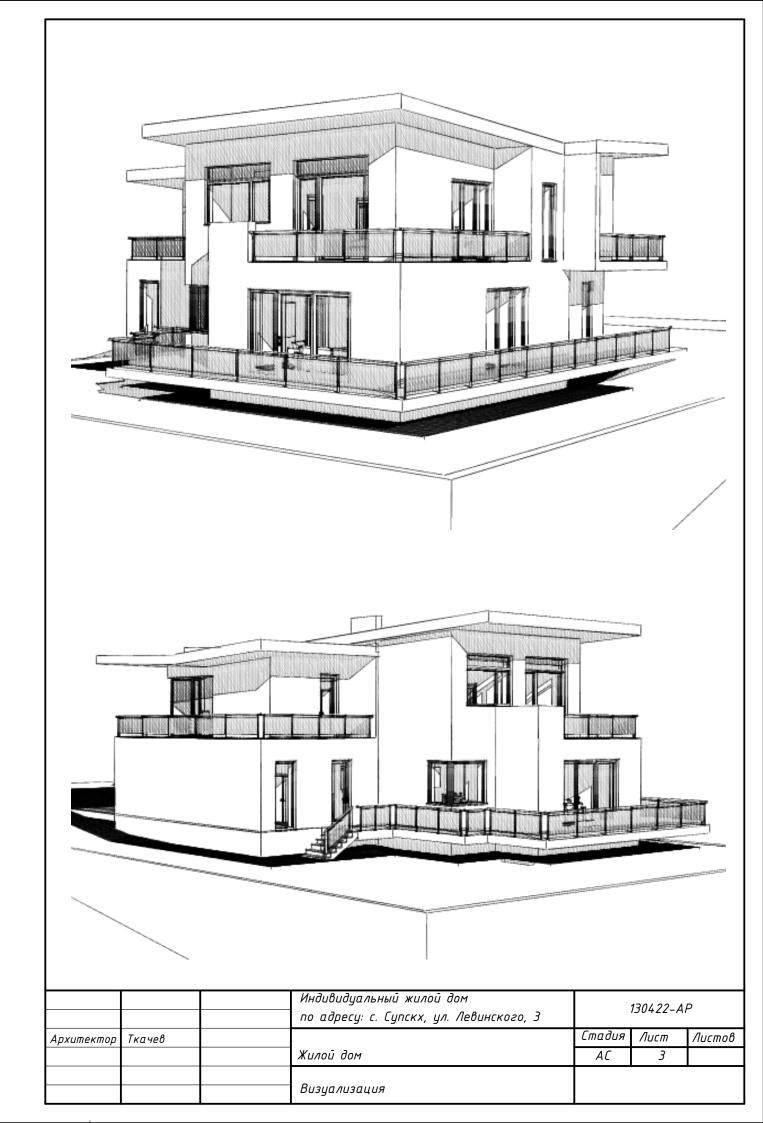

## ГЕНПЛАН

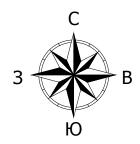

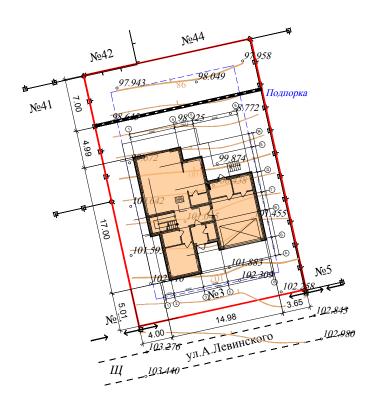

# УСЛОВНЫЕ ОБОЗНАЧЕНИЯ:

——— - Г<u>г</u>

- Граница участка землепользования


\_\_\_\_\_


- зона 3-х метрового отступа от границы з.у.




- Проектируемый жилой дом


		Индивидуальный жилой дом по адресу: с. Супскх, ул. Левинского, 3		130422-AP			
Архитектор	Ткачев			Стадия	Лист	Листов	
			Жилой дом	ΑC	4		
			_				
			I енплан				

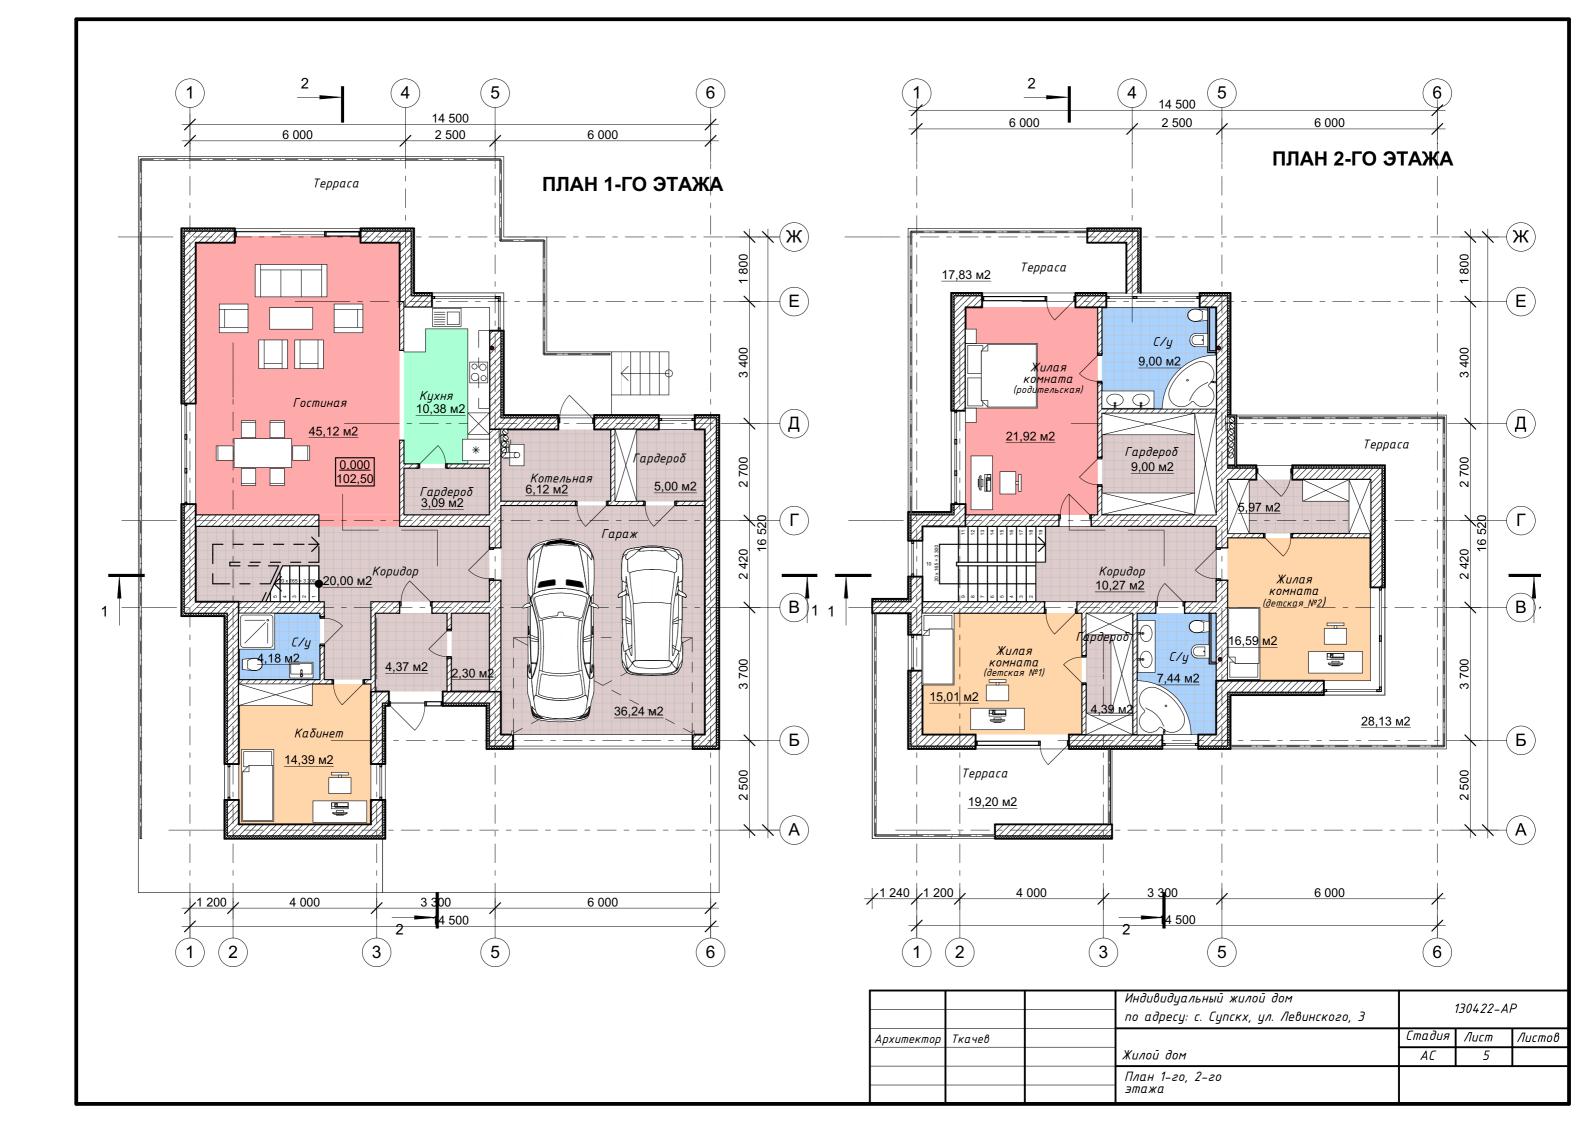


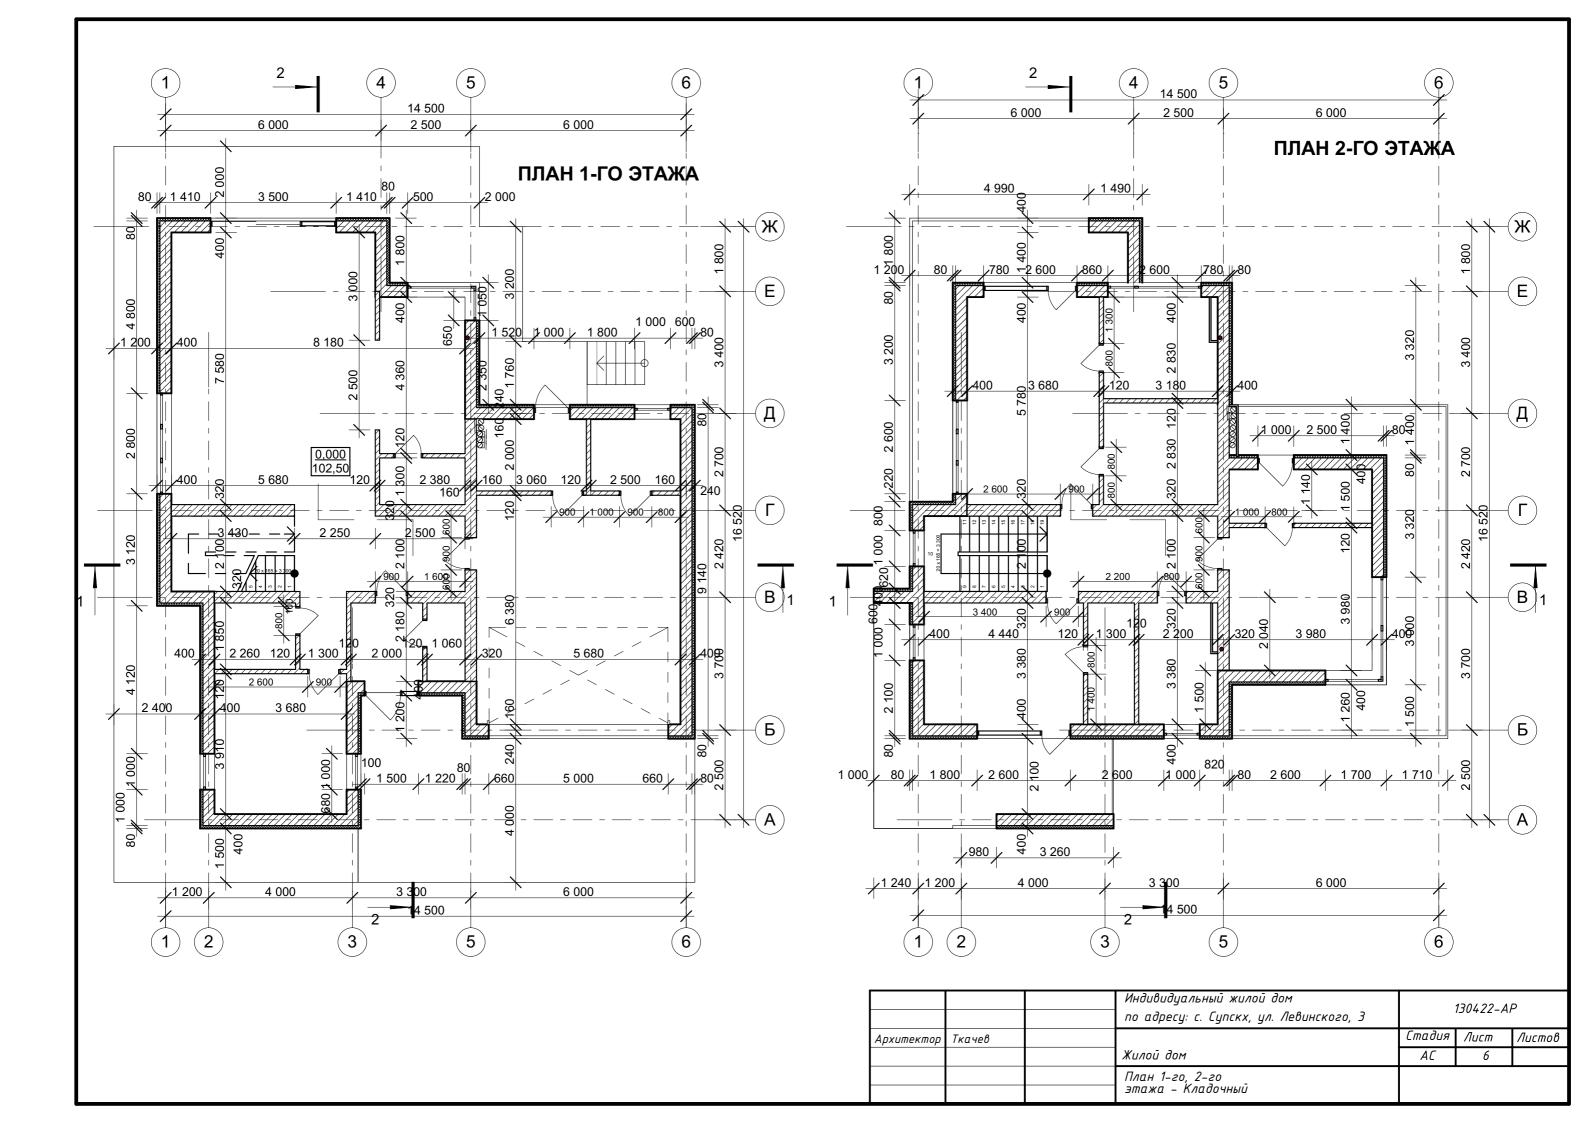


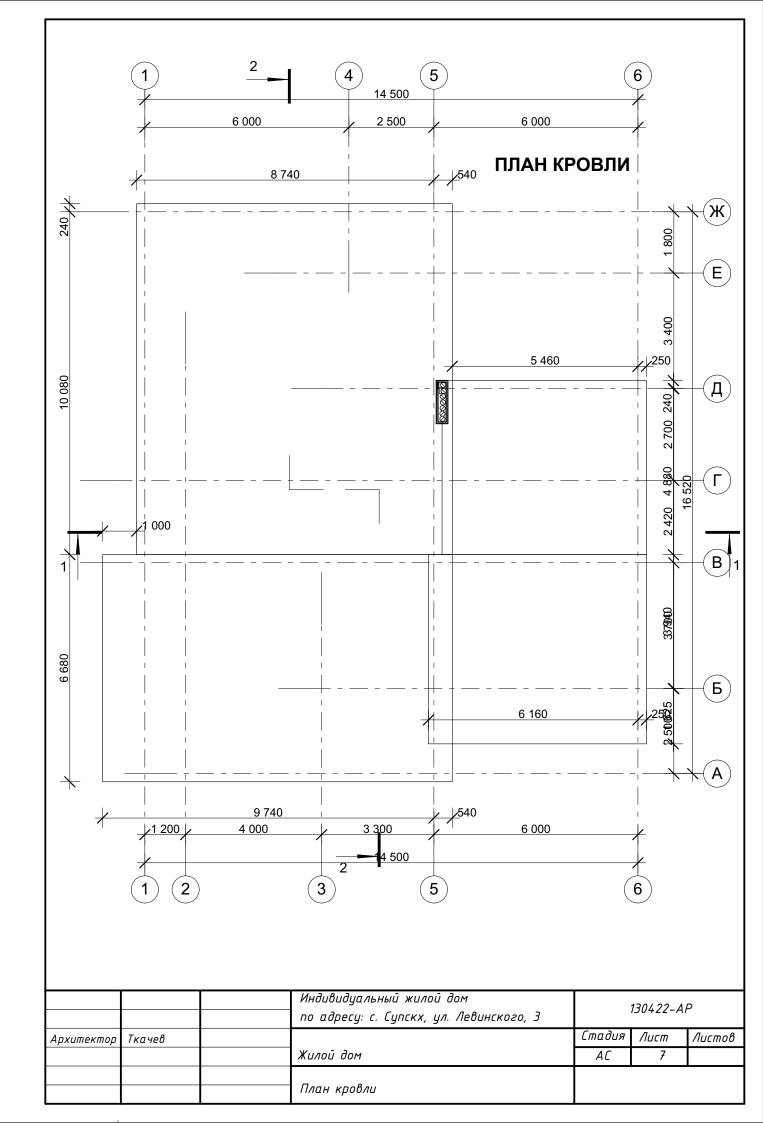



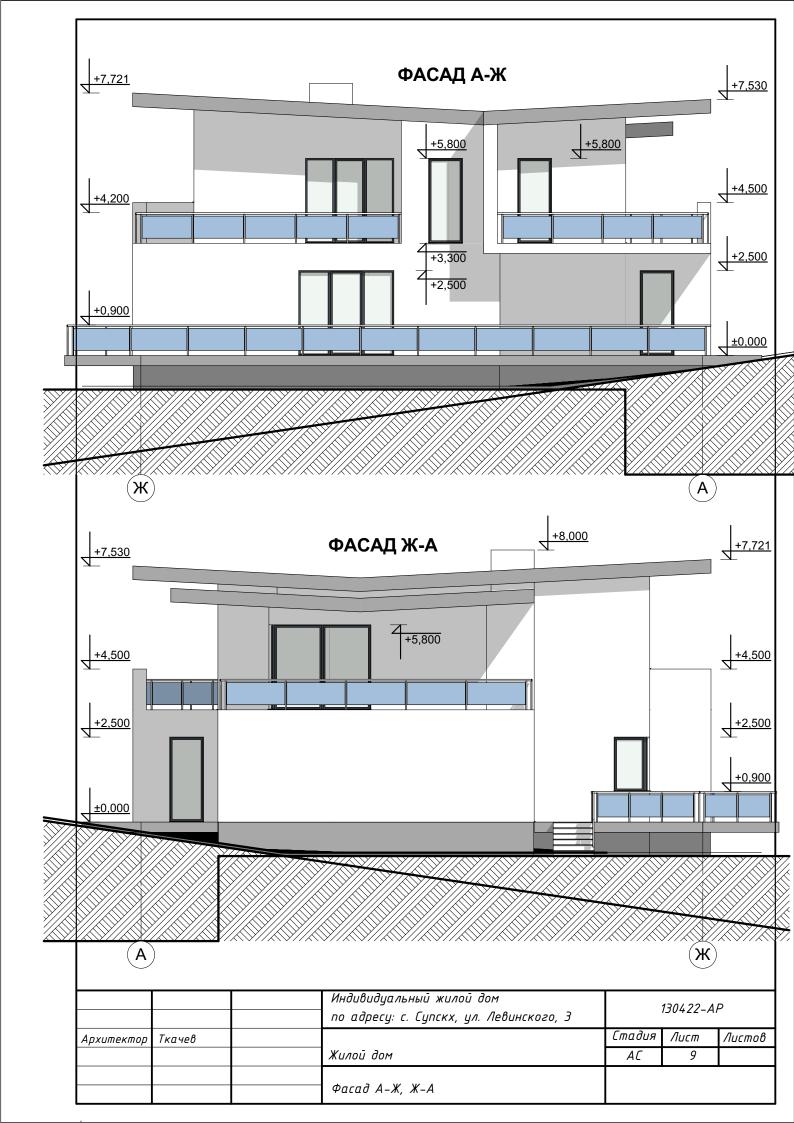

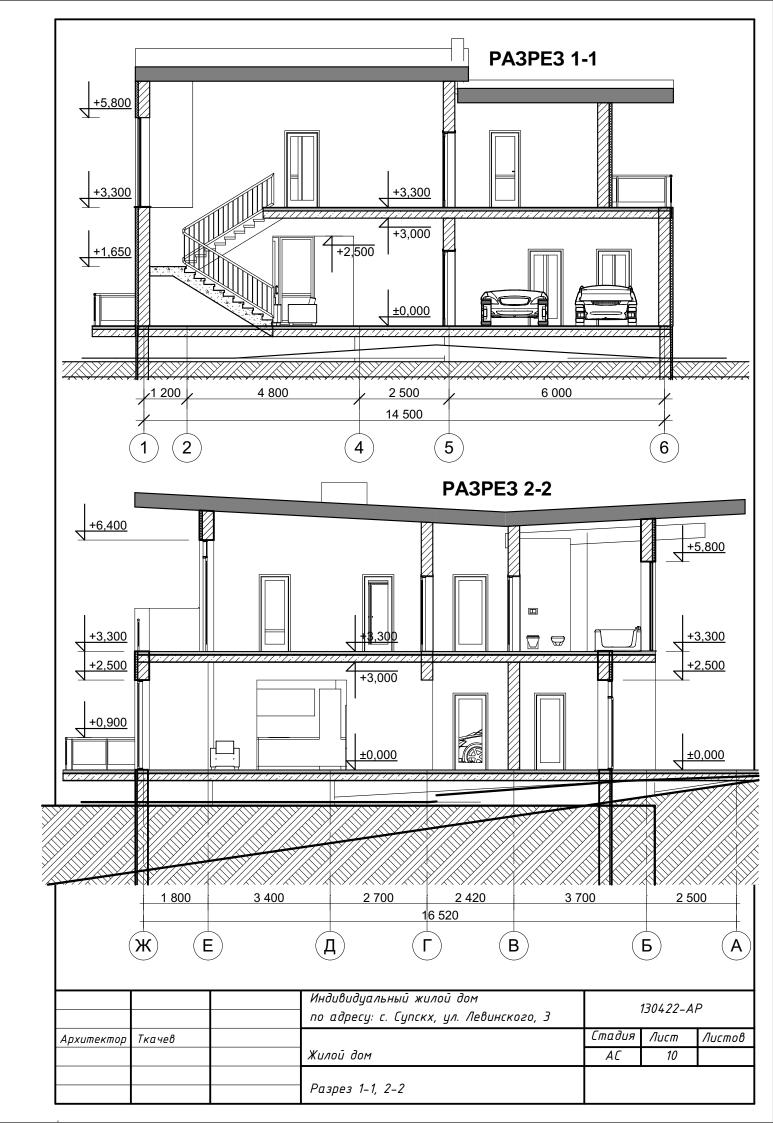

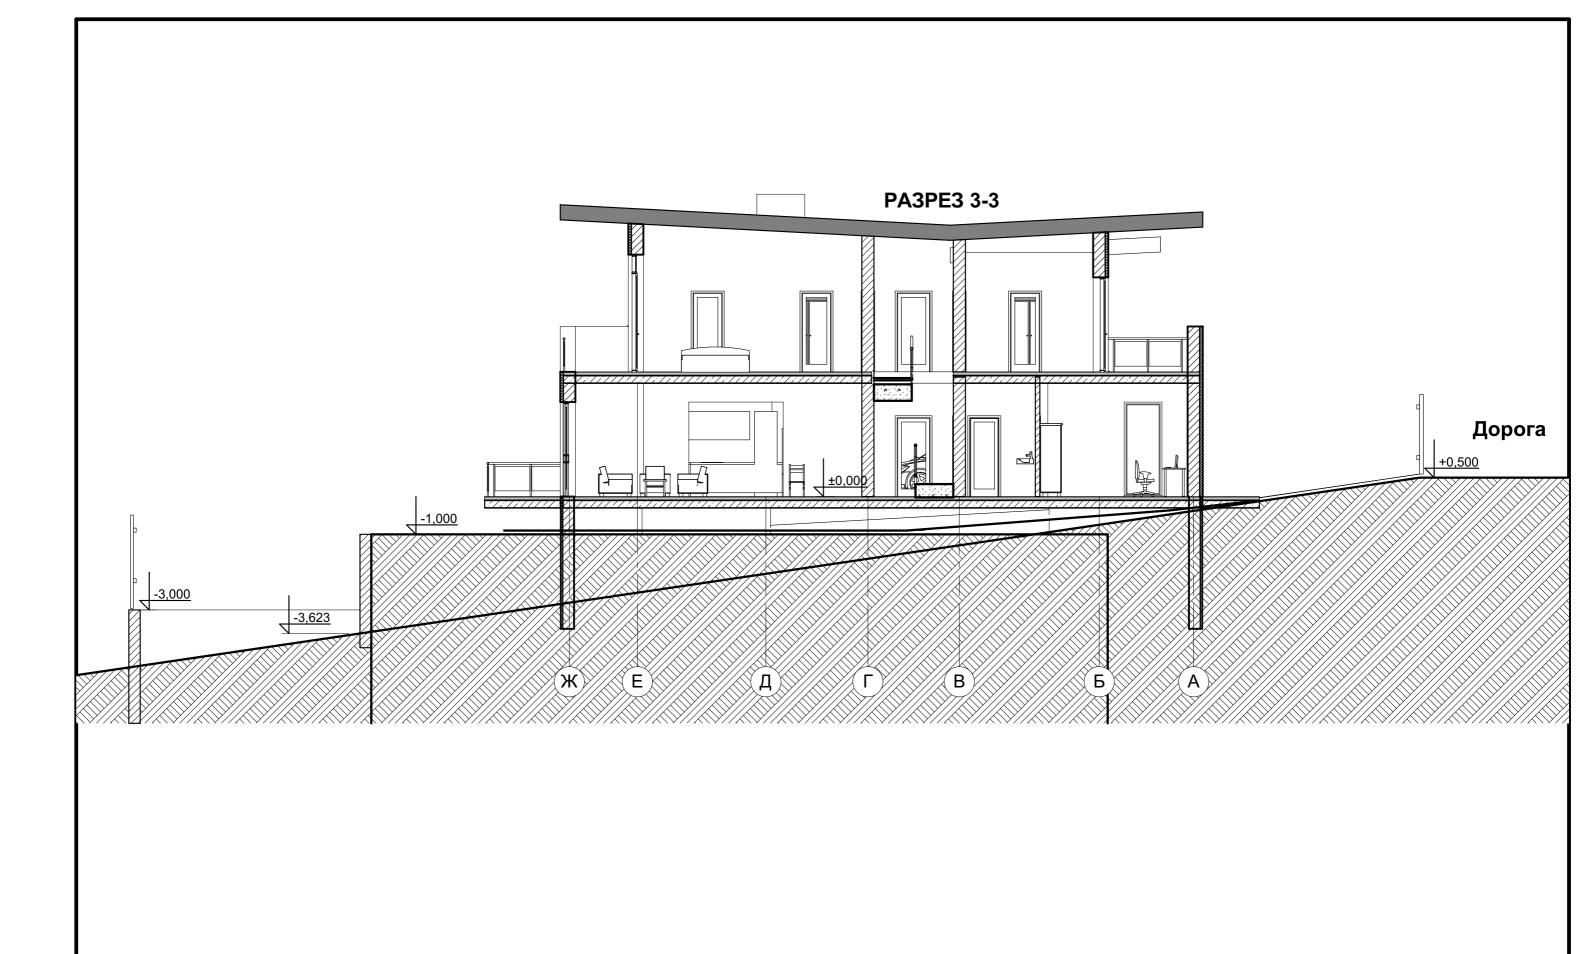

		Индивидуальный жилой дом по адресу: с. Супскх, ул. Левинского, З	130422-AP		D
Архитектор	Ткачев	L	Стадия	Лист	Листов
		Жилой дом	ΑC	11	
		Разрез 3–3			